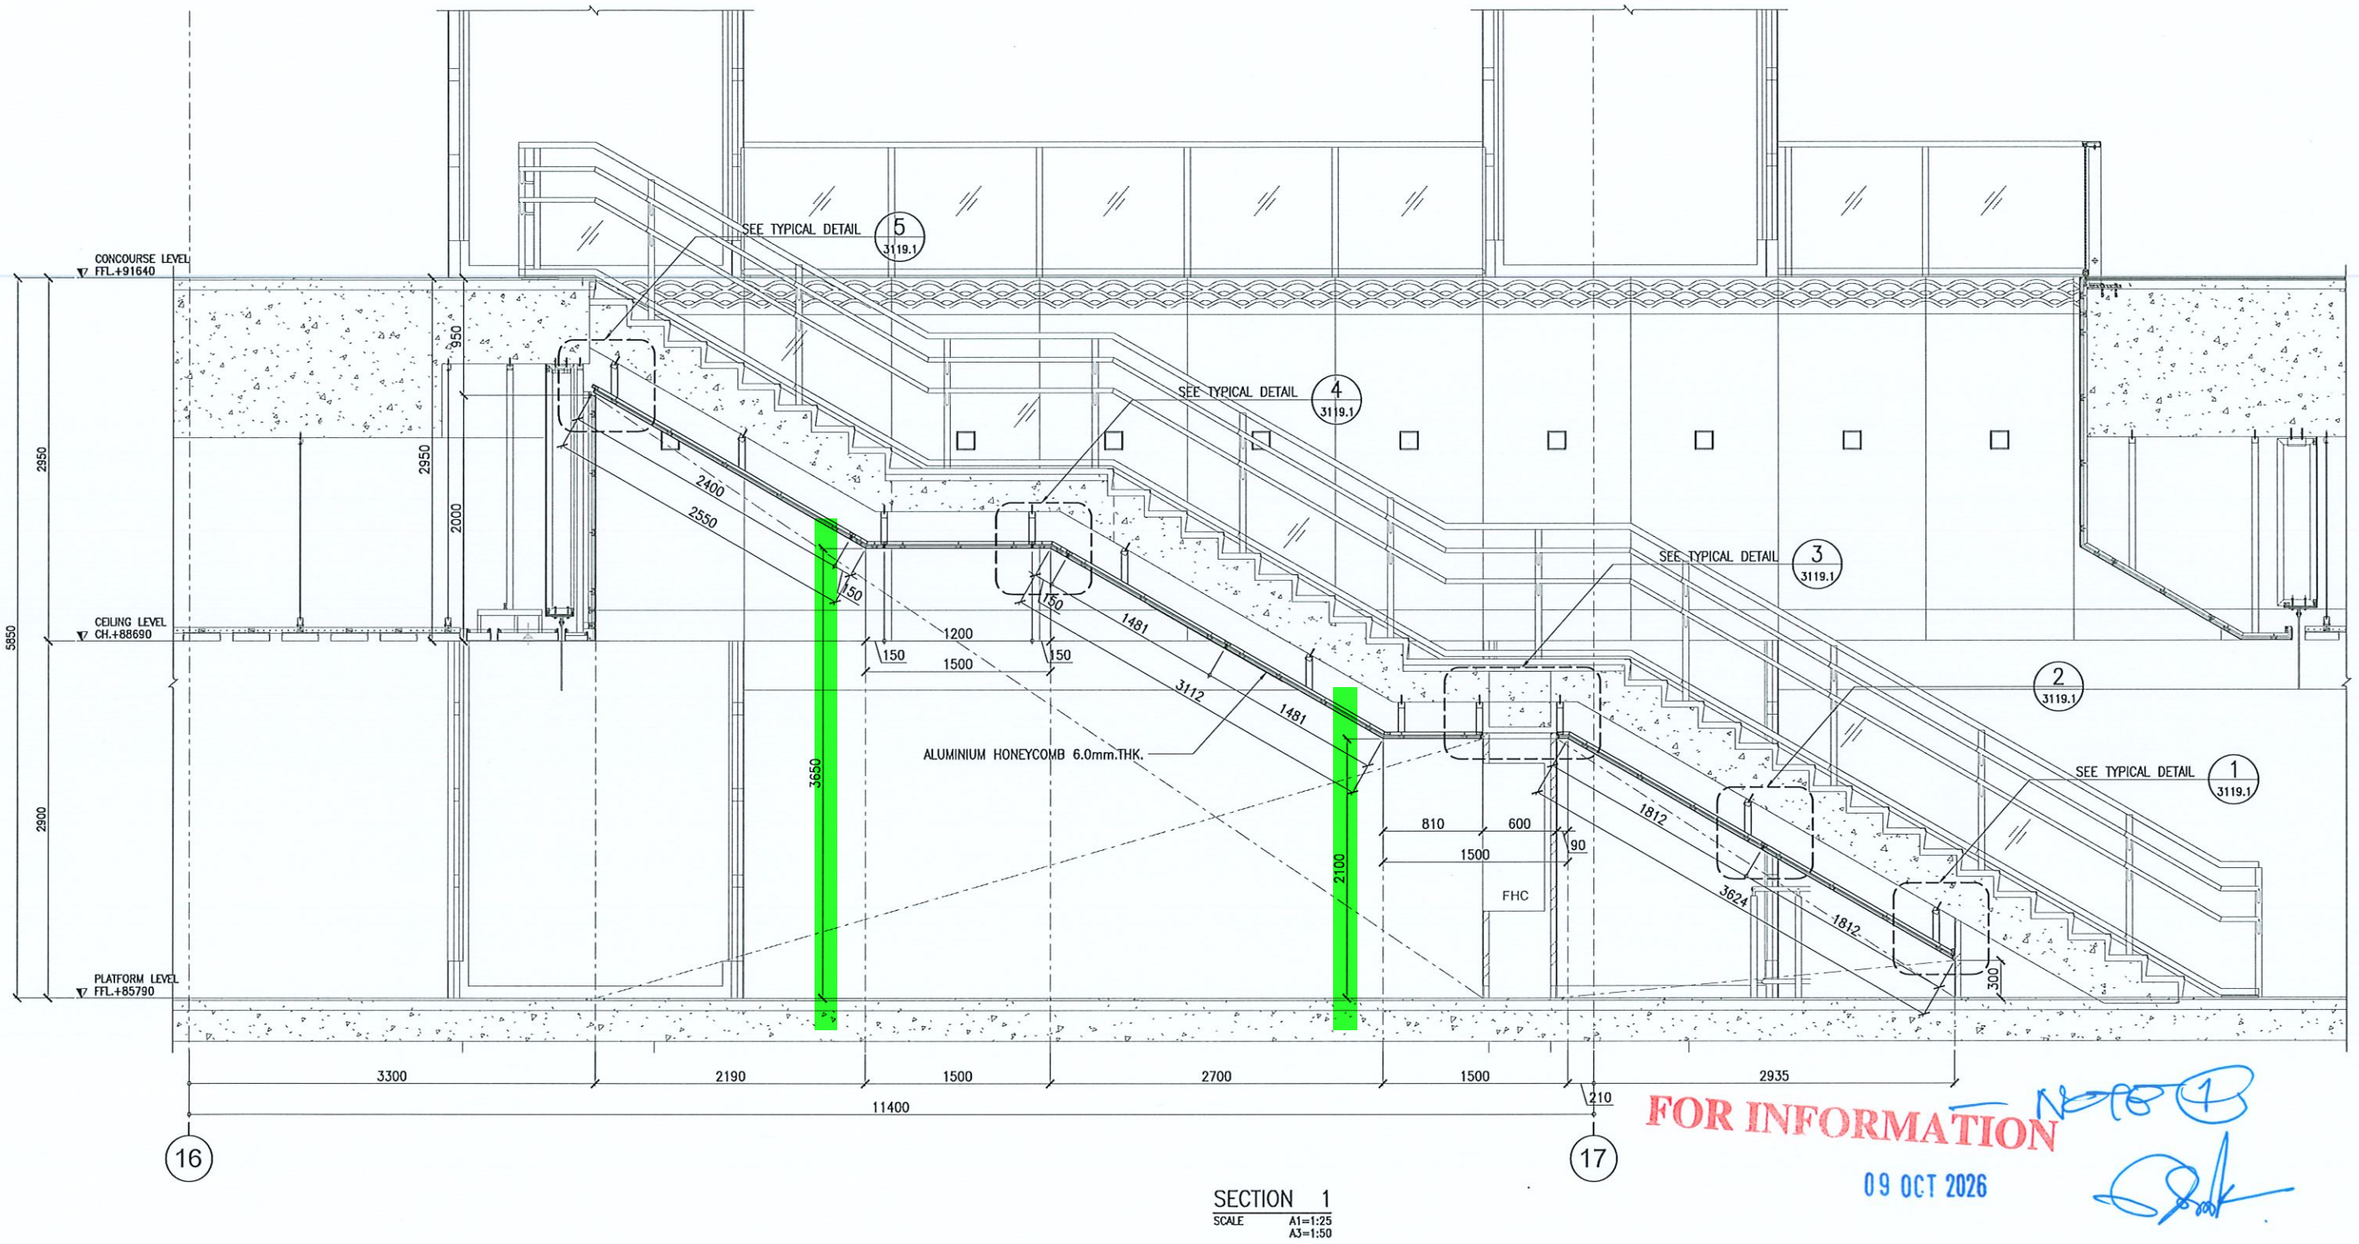



SECTION 1

SCALE A1=1:25
A3=1:50

FOR INFORMATION

09 OCT 2026

FAMELINE

FAMELINE PRODUCTS CO., LTD.

WARNING : ALL DESIGN AND DRAWING ARE PROPERTY OF FAMELINE PRODUCTS CO.,LTD. CANNOT USED WITHOUT THEIR PERMISSION

KINGDOM OF THAILAND
MINISTRY OF TRANSPORT
MASS RAPID TRANSIT AUTHORITY OF THAILAND

EMPLOYER'S REPRESENTATIVE:
PMCSC1
THE PROJECT MANAGEMENT AND CONSTRUCTION SUPERVISION CONSULTANT 1 (PMCSC1) FOR THE MRT PURPLE LINE PROJECT TAO PUN - RAT BURANA (KANCHANAPISEK ROAD) SECTION

CONTRACTOR : CKST-PL JOINT VENTURE
STECON
DESIGNER :
AECOM
GFE The Geotechnical Expert

| | | | | | | | | | | |
|---|---|---|---|---|---|---|---|---|---|---|
| DESIGNER | | SA | | | | | | | | |
| DESIGN CHECKED | | UY | | | | | | | | |
| PROJECT MANAGER | | PP | A | 19-03-2026 | FIRST ISSUED | TA | KEN | MK | | |
| | | | REV. | DATE | REVISIONS | DWG. | CHK. | APP. | | |

PMCSC1 WORKING DRAWING REVIEW

| | |
|---|---|
| 1 = NONO | SIGN : |
| 2 = NONO W COMMENT | NAME : |
| 3 = SOO | POSITION : |
| 4 = REJECTED | DATE : |

PURPLE LINE PROJECT

CONTRACT 1 : UNDERGROUND CIVIL WORKS

PP17 - PARLIAMENT HOUSE STATION
STAIR & ESCALATORS - ST.2 (PART 2)
SECTION 1

| SCALE : | UNITS : | DATE : | STATUS : | DRAWING NO. | REVISION : | SHEET NO. |
|---|---|---|---|---|---|---|
| A1 = 1:25<br>A3 = 1:50 | mm. | 19-03-2026 | W | 1-PP17-AR-3117-01 | A | - |

CAD@SCM-Cad D:_Work_Fameline\68-10-16 PURPLE LINE\PP17\work\PP17_ST.2\W-1-PP17-AR-ST.2_Part2_20260319.dwg [ST2-2] Mar 18, 2026-9:52pm